


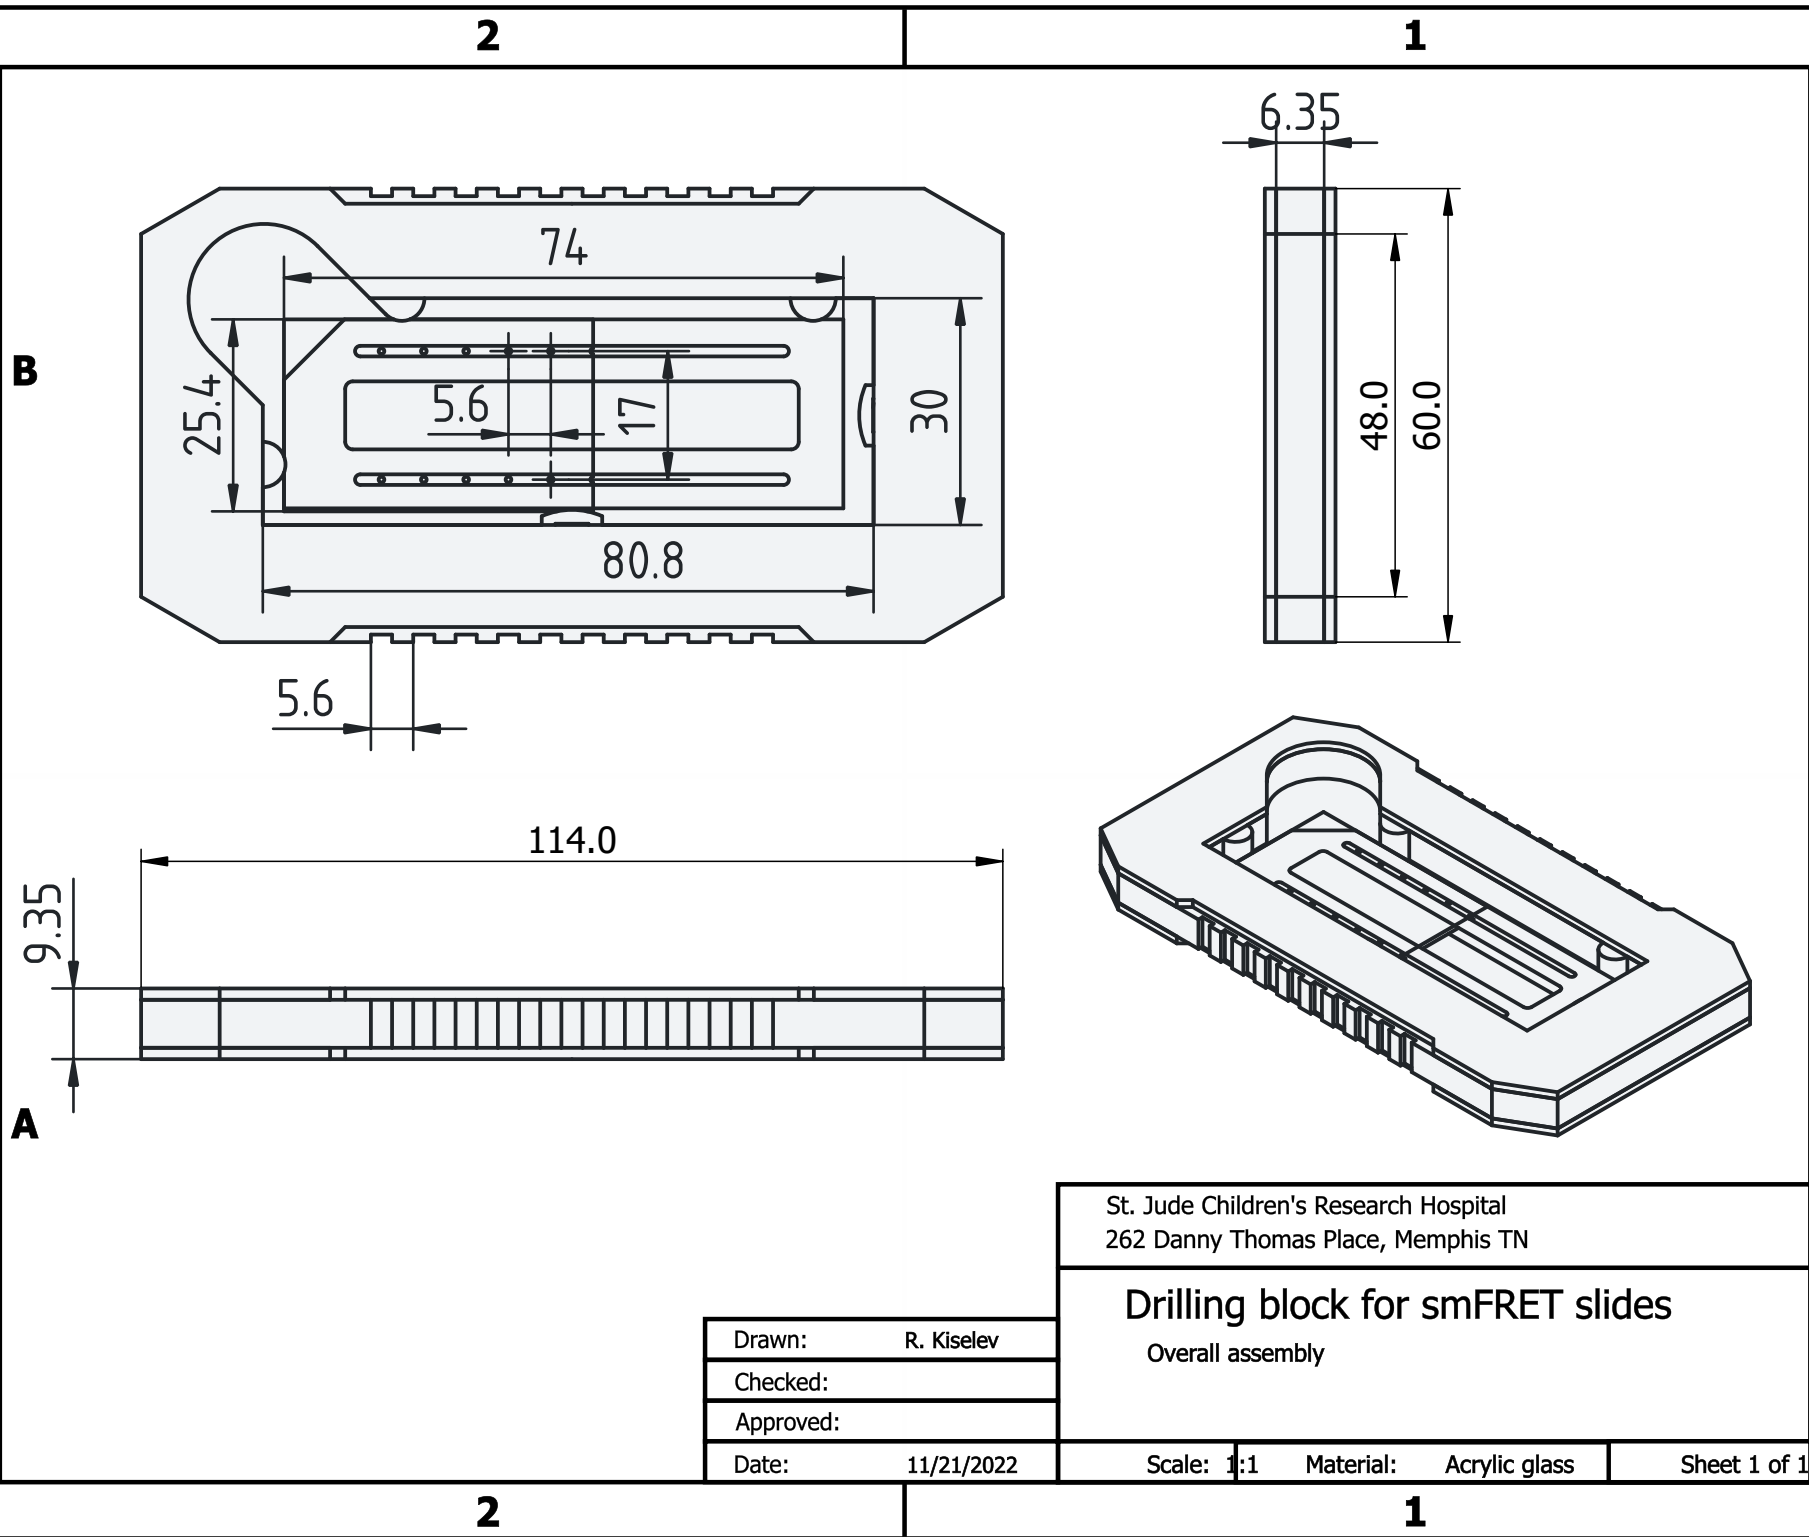

St. Jude Children's Research Hospital
262 Danny Thomas Place, Memphis TN

Drilling block for smFRET slides
Overall assembly

Drawn:	R. Kiselev
Checked:	
Approved:	
Date:	11/21/2022